


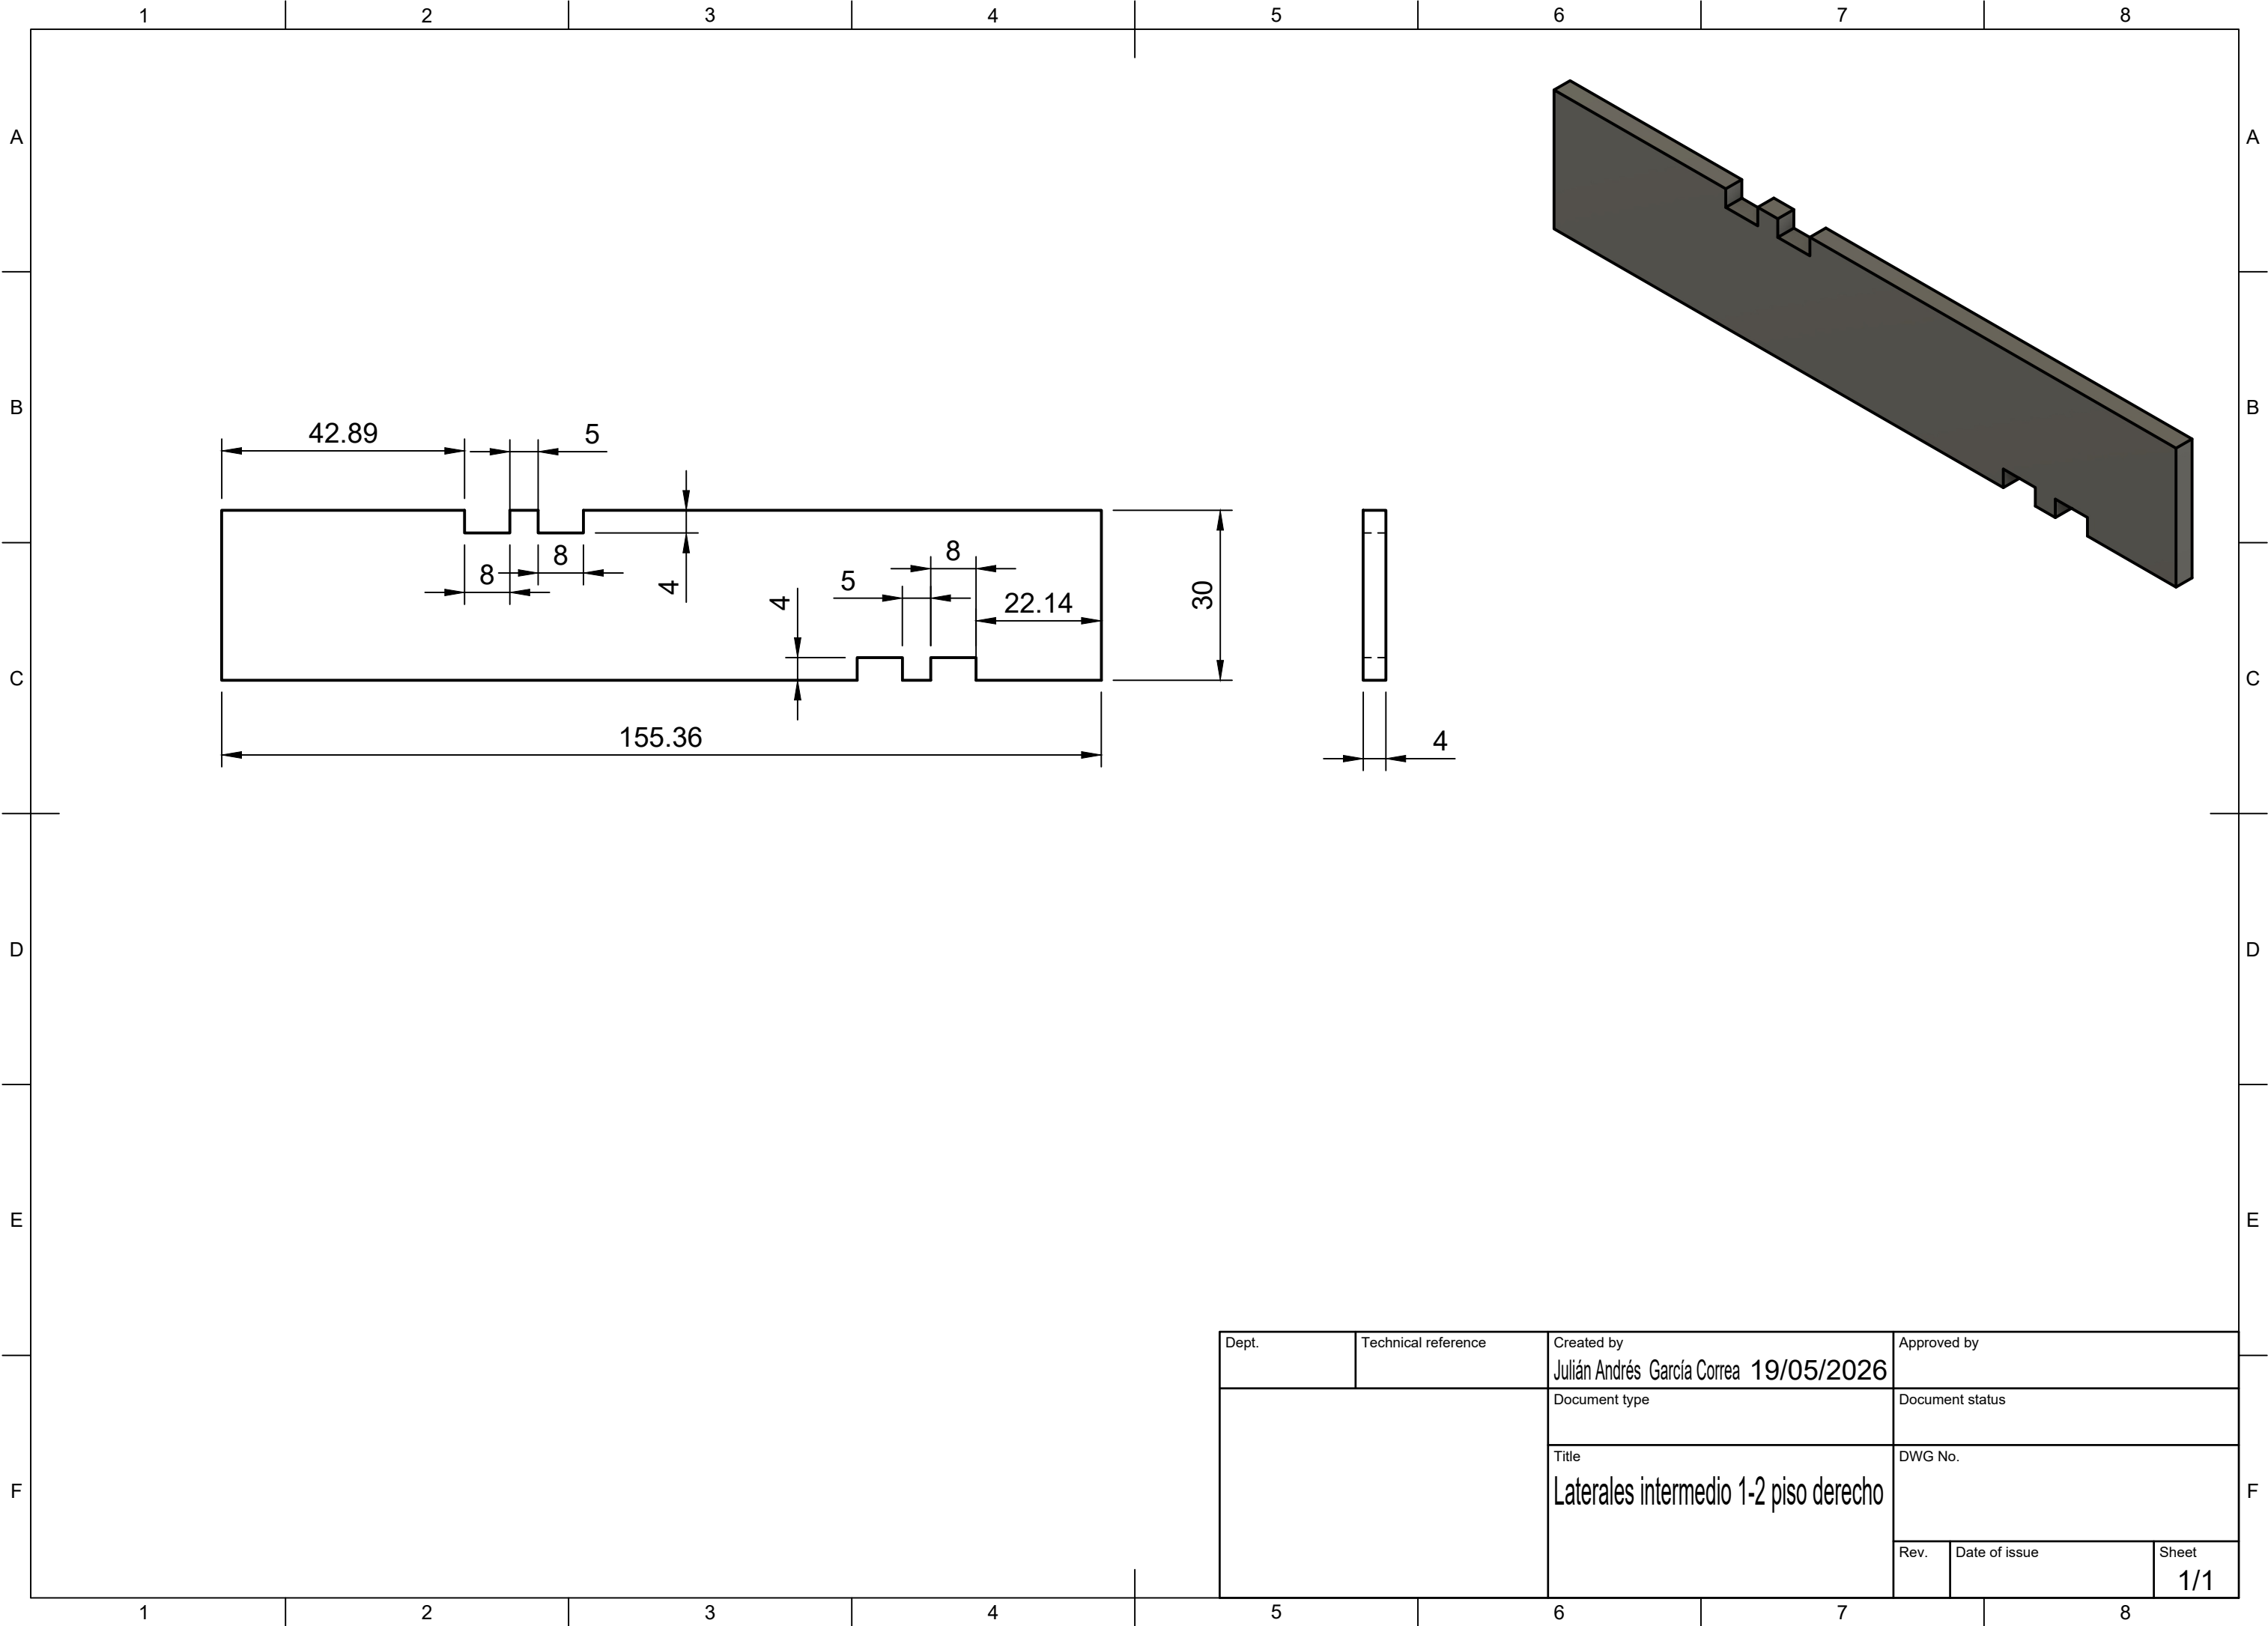

Dept.	Technical reference	Created by Julián Andrés García Correa 19/05/2026	Approved by	
		Document type	Document status	
		Title Laterales intermedio 1-2 piso derecho	DWG No.	
		Rev.	Date of issue	Sheet 1/1